


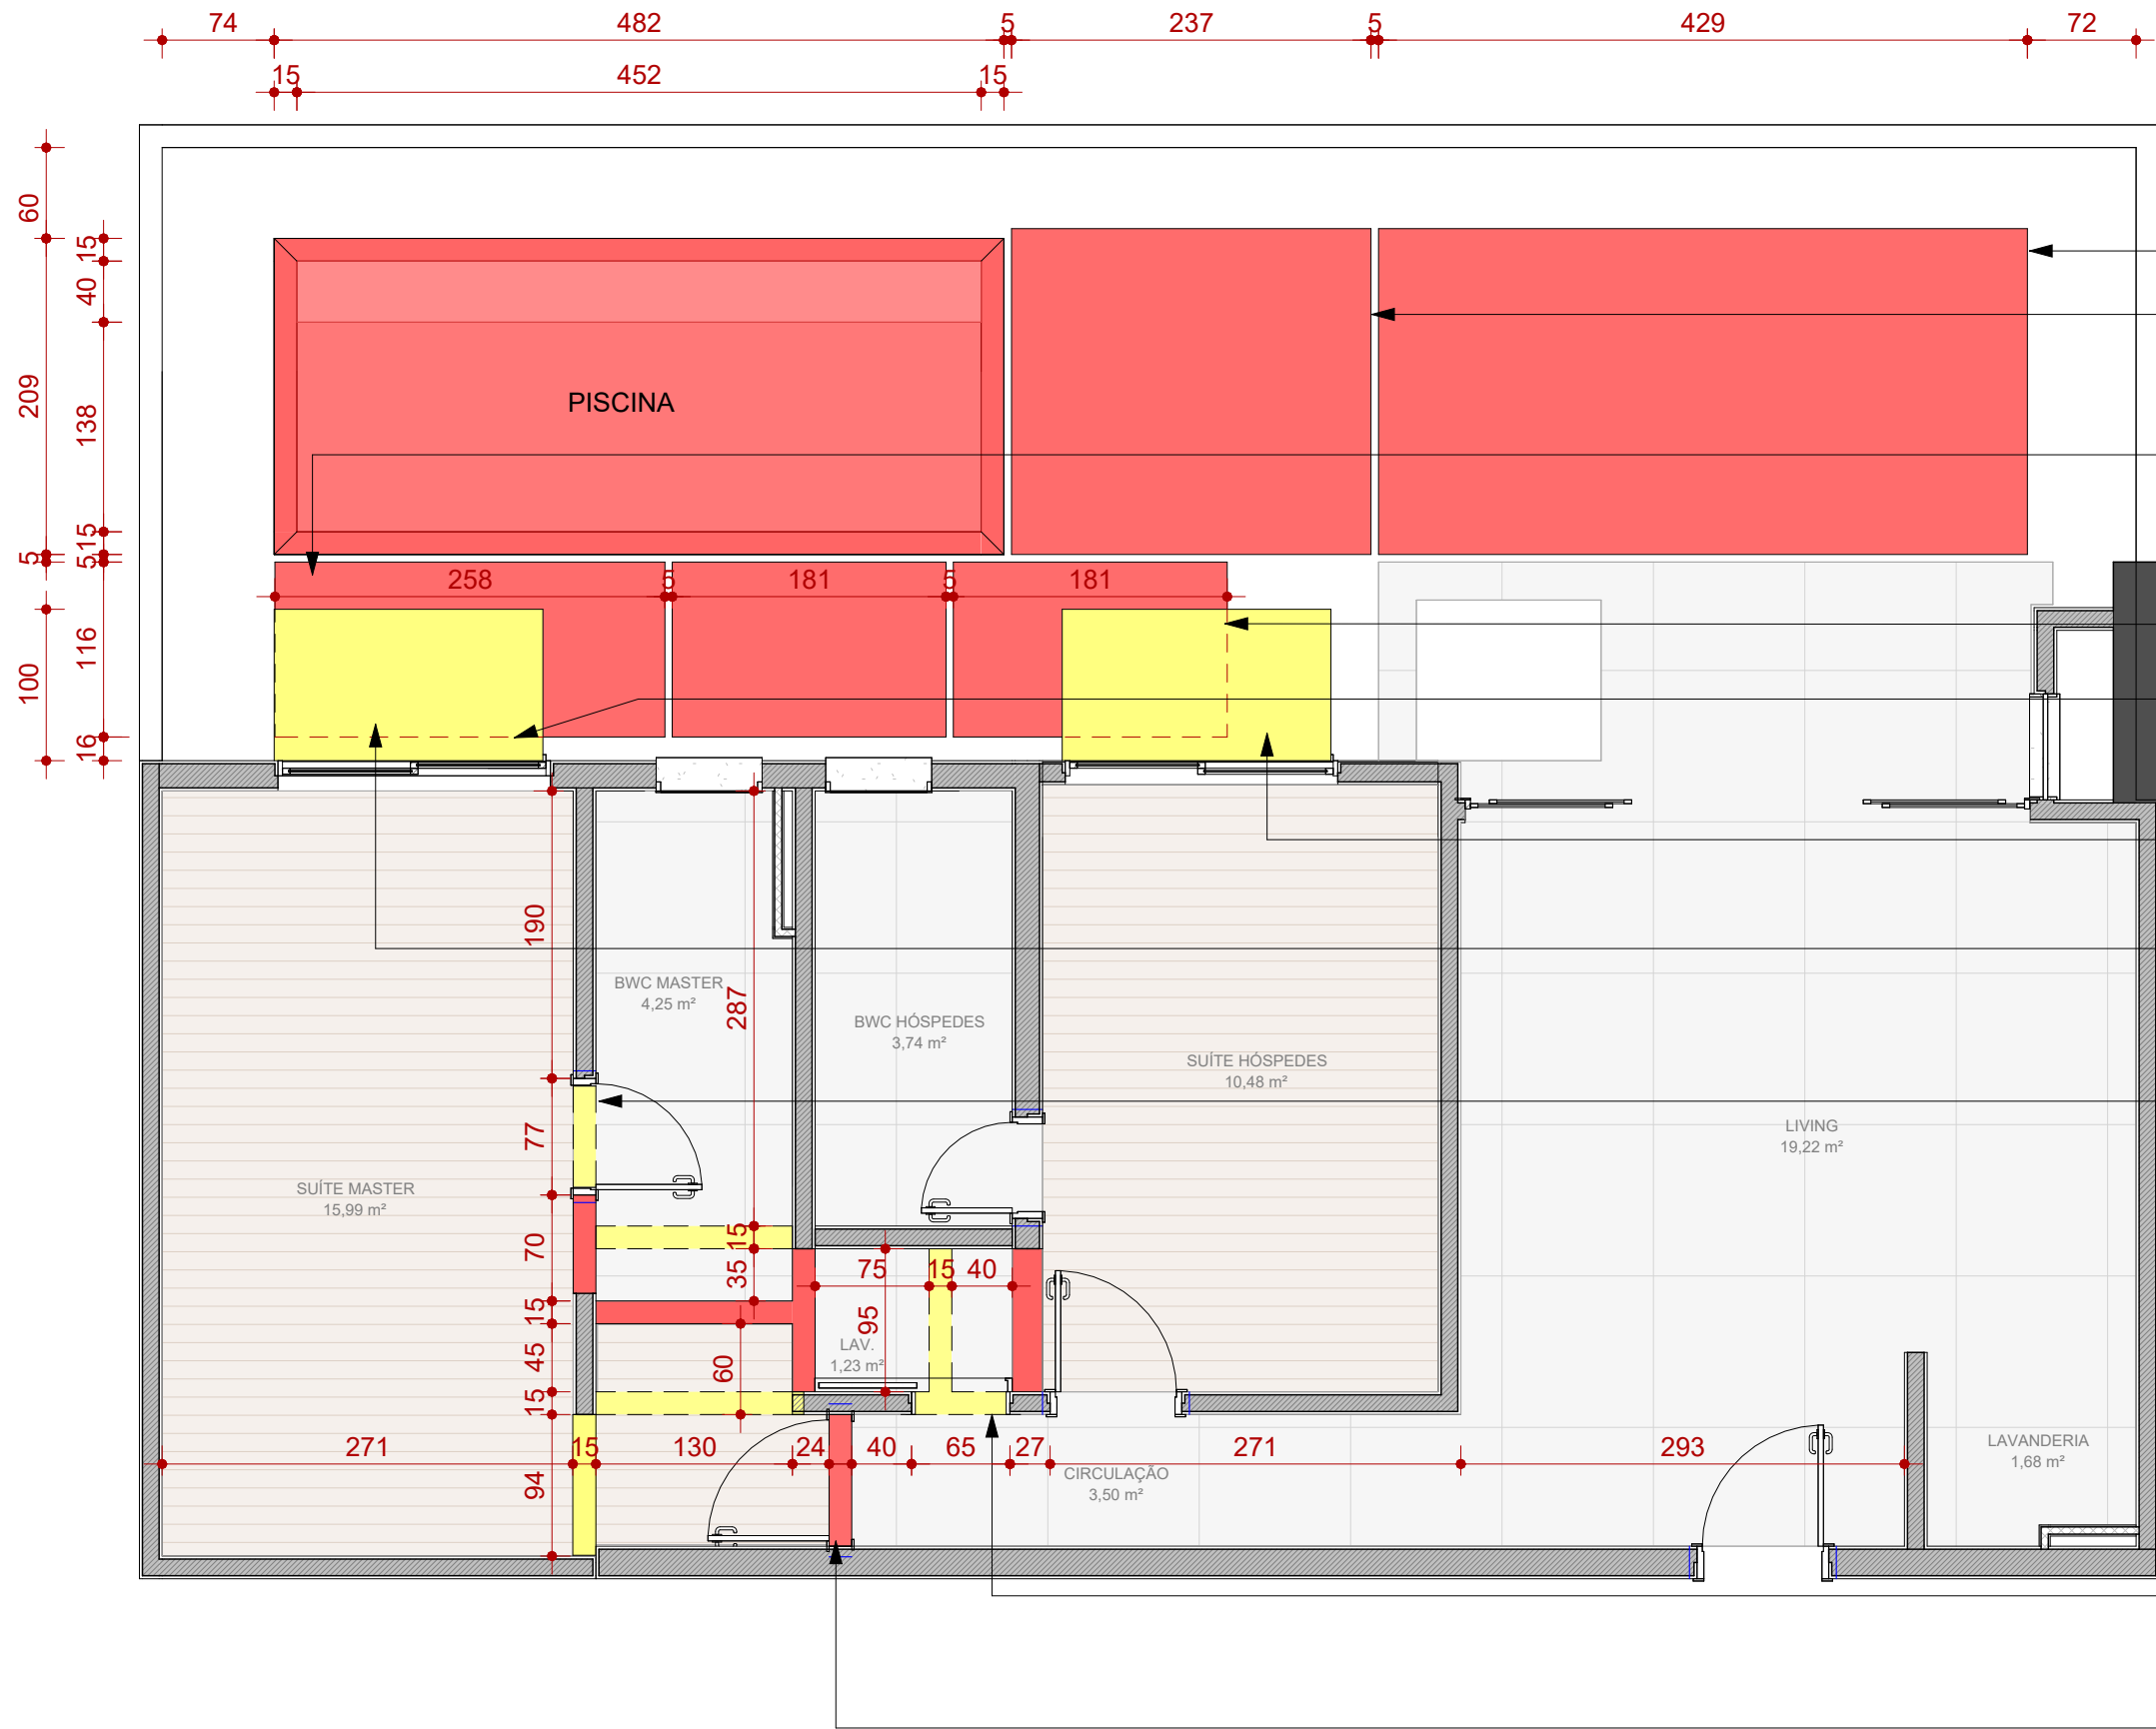

LEGENDA DEMOLIR/CONSTRUIR

- PAREDE A SER CONSTRUÍDA
- PAREDE A SER DEMOLIDA, H= 210
- PAREDE EM ALVENARIA A SER MANTIDA

Nº	DATA	DESCRIÇÃO
REVISÕES		

Projeto Arquitetônico | MAUI

CONTEÚDO | PLANTA DE DEMOLIR E CONSTRUIR APT 109

INSCRIÇÃO IMOBILIÁRIA 0 ÁREA DO LOTE 0,00 m²

ENDEREÇO DA OBRA
RÓD. JORNALISTA MANOEL DE MENEZES, Nº 0, BARRA DA LAGOA,
FLORIANÓPOLIS/SC, CEP:88.061-701

PROPRIETÁRIO(S)
Cliente
CPF/CNPJ - 40.503.642/0001-28

ASSINATURA

RESPONSÁVEL TÉCNICO PROJETO
Fábio Silva
ARQUITETO E URBANISTA | CAU - A131393-2

ASSINATURA

RESPONSÁVEL TÉCNICO EXECUÇÃO
Nome Responsável Técnico
ENGENHEIRO CREA/SC: 000.000.000-00

ASSINATURA

Tel.: (00) 00000 0000
E-mail: email@execução.eng.br


26/06/2026

PLANTA DE DEMOLIR E
CONSTRUIR

ESCALA

1 : 50

1 DEMOLIR E CONSTRUIR
1 : 50

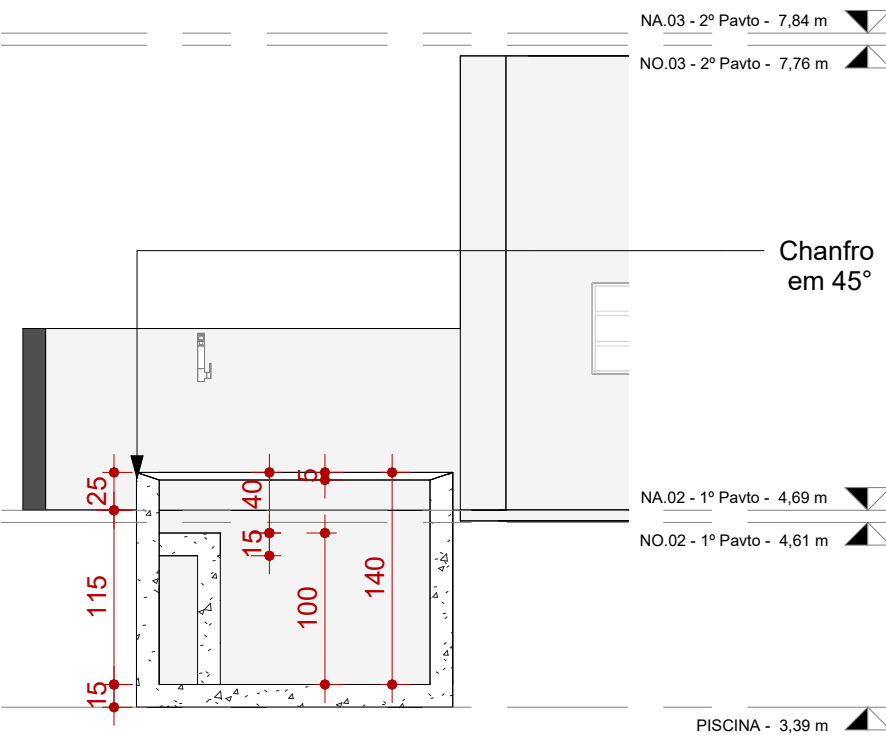

2 CORTE 02
1 : 50



:@dhousebr

:+55 (48) 3307-4616

:DHOUSE.ARQ.BR

D'HOUSE