



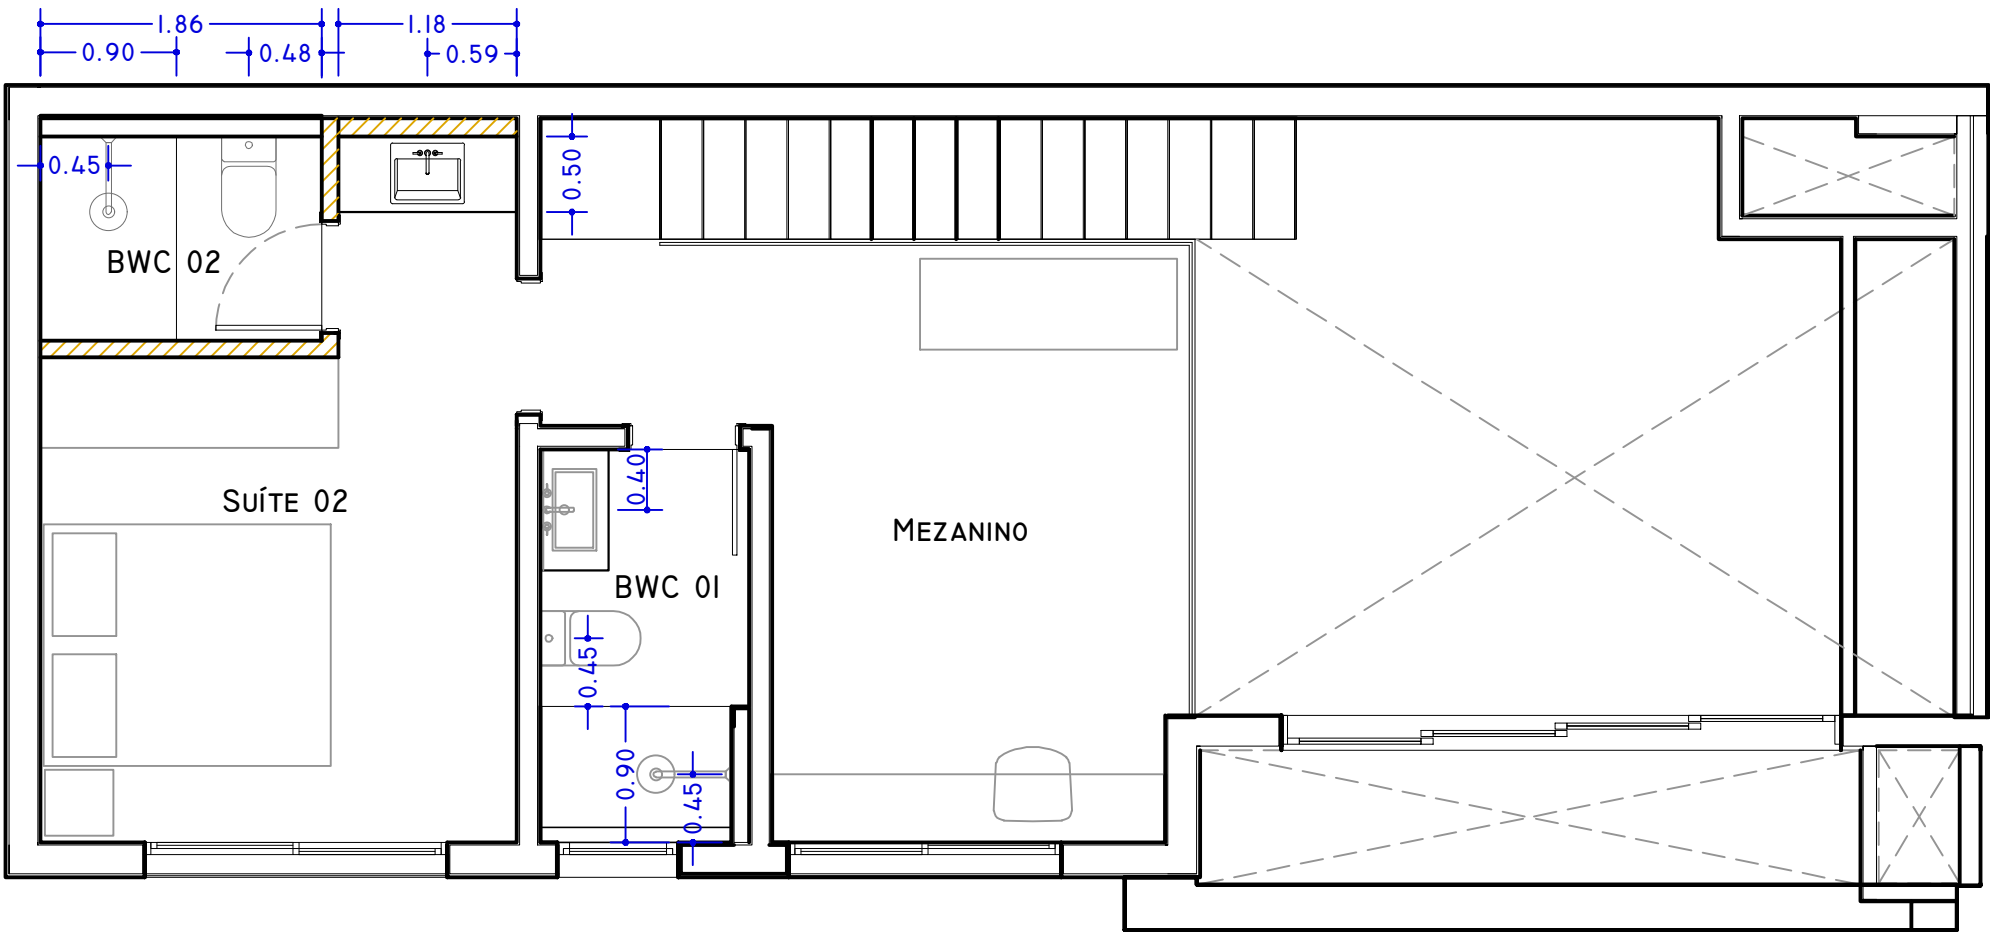

PLANTA BAIXA - PONTOS HIDRÁULICA
UNIDADE 204
AP 1
prop. LUIS FERNANDO M. MAX

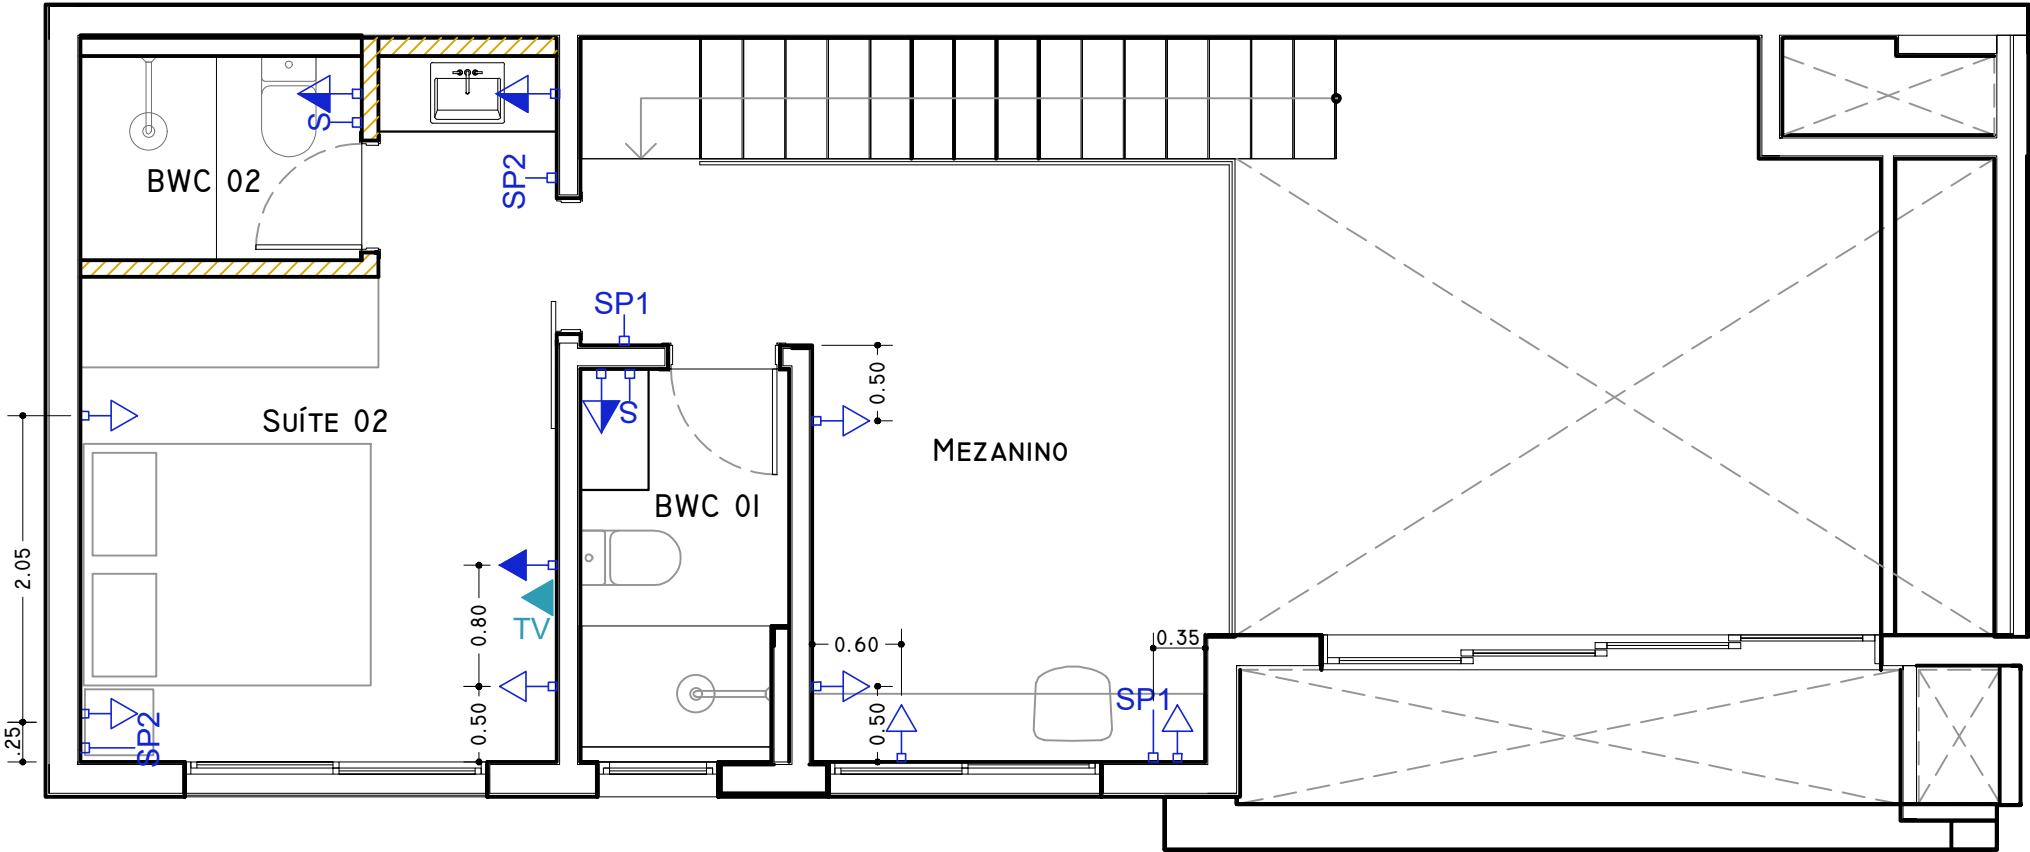

LEGENDA	
S	INTERRUPTOR SIMPLES (H=1.20)
Sp	INTERRUPTOR PARALELO (H=1.20)
△	TOMADA BAIXA (H=0.40)
△	TOMADA MÉDIA (H=1.20)
△	TOMADA ALTA/TV (H=1.50)
TV	ANTENA (SKY/TV H=1.50)

PLANTA BAIXA - PONTOS ELÉTRICA
UNIDADE 204
AP 1
prop. LUIS FERNANDO M. MAX